

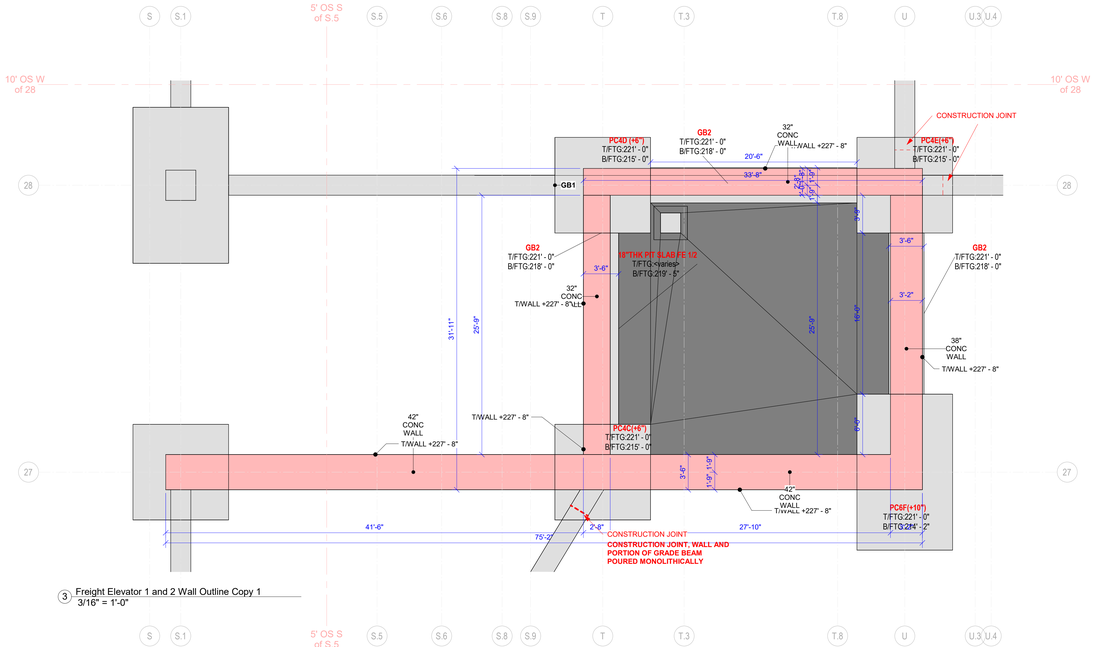



3 Freight Elevator 1 and 2 Wall Outline Copy 1
3/16" = 1'-0"

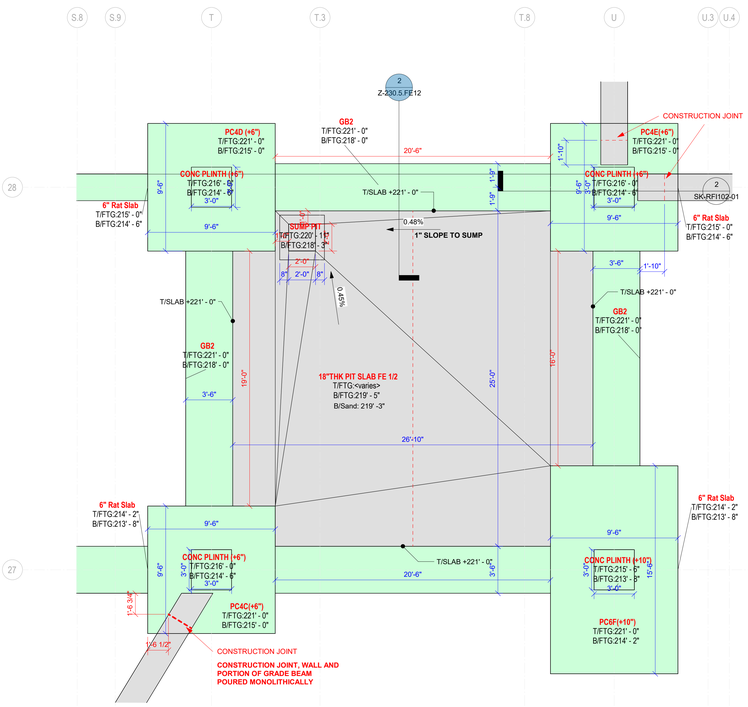


1 Freight Elevator 1 and 2 Foundation Outline Copy 1
1/4" = 1'-0"

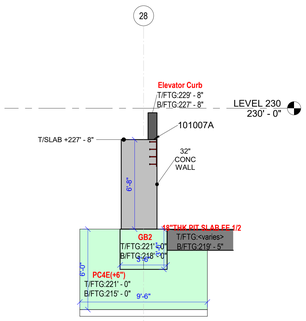

2 Section 327 Copy 2 Copy 3
1/4" = 1'-0"

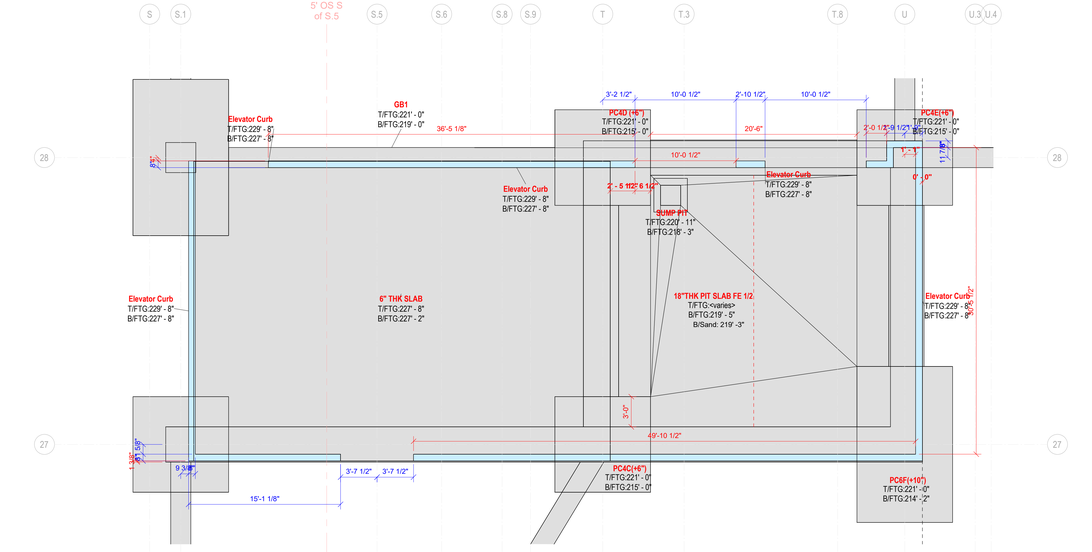

5 T/28 Elevator Curb Plan Copy 1
3/16" = 1'-0"

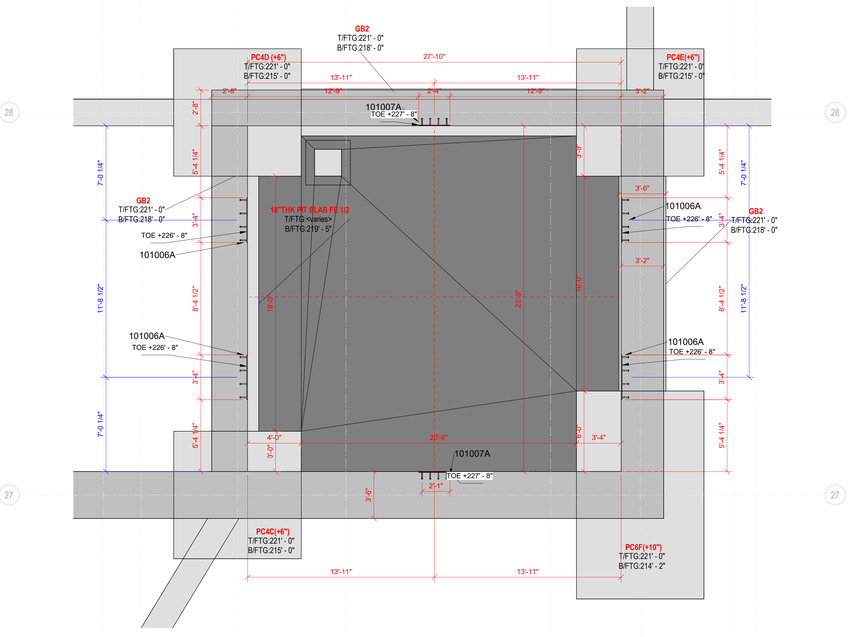

4 Freight Elevator 1 and 2 Embed Plan Copy 1
1/4" = 1'-0"

PCL CONSTRUCTION | WEBCOR
A JOINT VENTURE
San Francisco, CA 94105
WEBCOR CONCRETE
1751 Harbor Bay Parkway, Suite 200
Alameda, CA 94502
Phone: (510) 748-1900
Fax: (510) 748-7800

LOS ANGELES CONVENTION CENTER
EXPANSION + MODERNIZATION
1201 S.FIGUEROA ST. LOS ANGELES, CA 90015

IMPORTANT NOTE:
THESE DRAWINGS ARE NOT INTENDED TO REPLACE THE DESIGN ARCHITECTURAL AND STRUCTURAL DRAWINGS. ALL DIMENSIONS, LOCATIONS, AND ELEVATIONS SHOWN ON THIS DRAWING ARE TO BE CHECKED ON-SITE AGAINST THE LATEST DESIGN AND DOCUMENTATIONS.

Revision Schedule

Rev. No.	Revision Description	Rev. Date

Reference Documents:

Drawn By:	DY
Date PDF Plotted:	10/6/2026 12:47:26 PM
WCG Job No.:	11088.70

TITLE:

Freight Elevator 1 and 2 OVERALL VIEW

SHEET NO:

Z-230.OV.FE12

SCALE: As indicated

Z-L.D.S DRAWING SHEET NO.
Where:
Z - ANSI SHOP DRAWING DESIGNATION
L - FLOOR LEVEL
D - DRAWING TYPE, WHERE:
0 - OVERALL PLAN
1 - SLAB PLAN
2 - SOFFIT/SUBGRADE PLAN
3 - VERTICAL PLAN
4 - CURB/TOPPING SLAB
5 - EMBED
6 - ELEVATIONS
7 - FINISH PLAN
8 - DETAILS
SL - SAFETY/LOGISTICS
PL - POINT LAYOUT
S - SHEET NO. (1,2,3, ETC if multiple pages)