

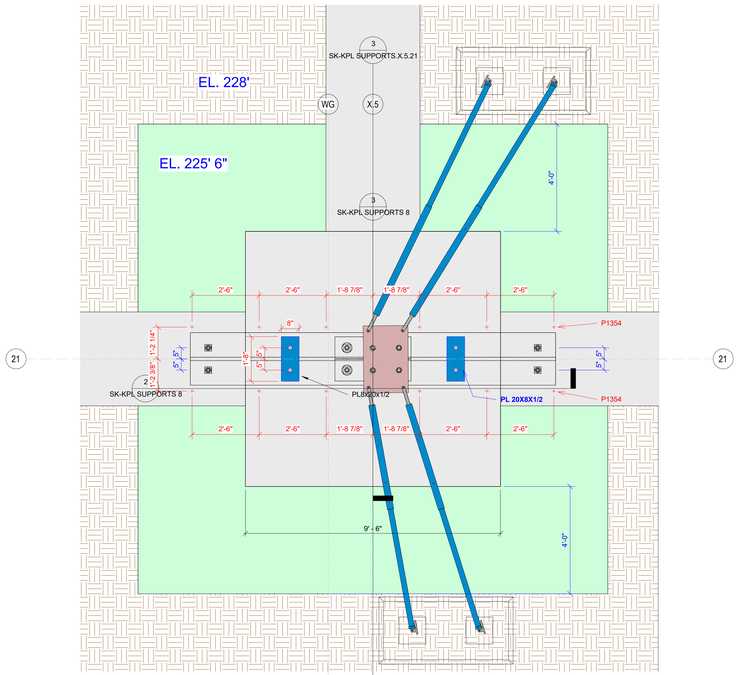



1 GL X.5/21 - LEVEL 223 Copy 2 Copy 1
1/2" = 1'-0"

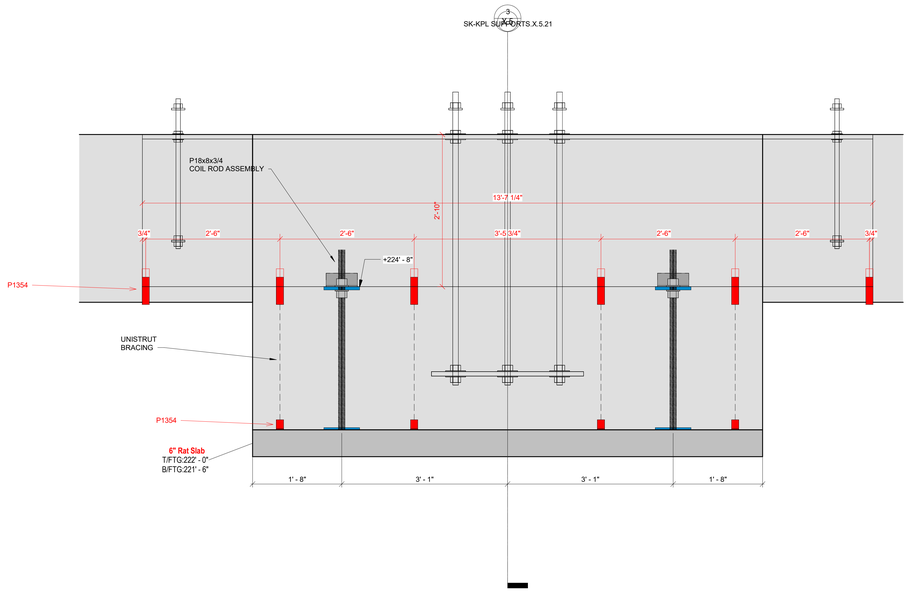


2 GL X.5/21 - E/W Copy 2 Copy 1
1" = 1'-0"

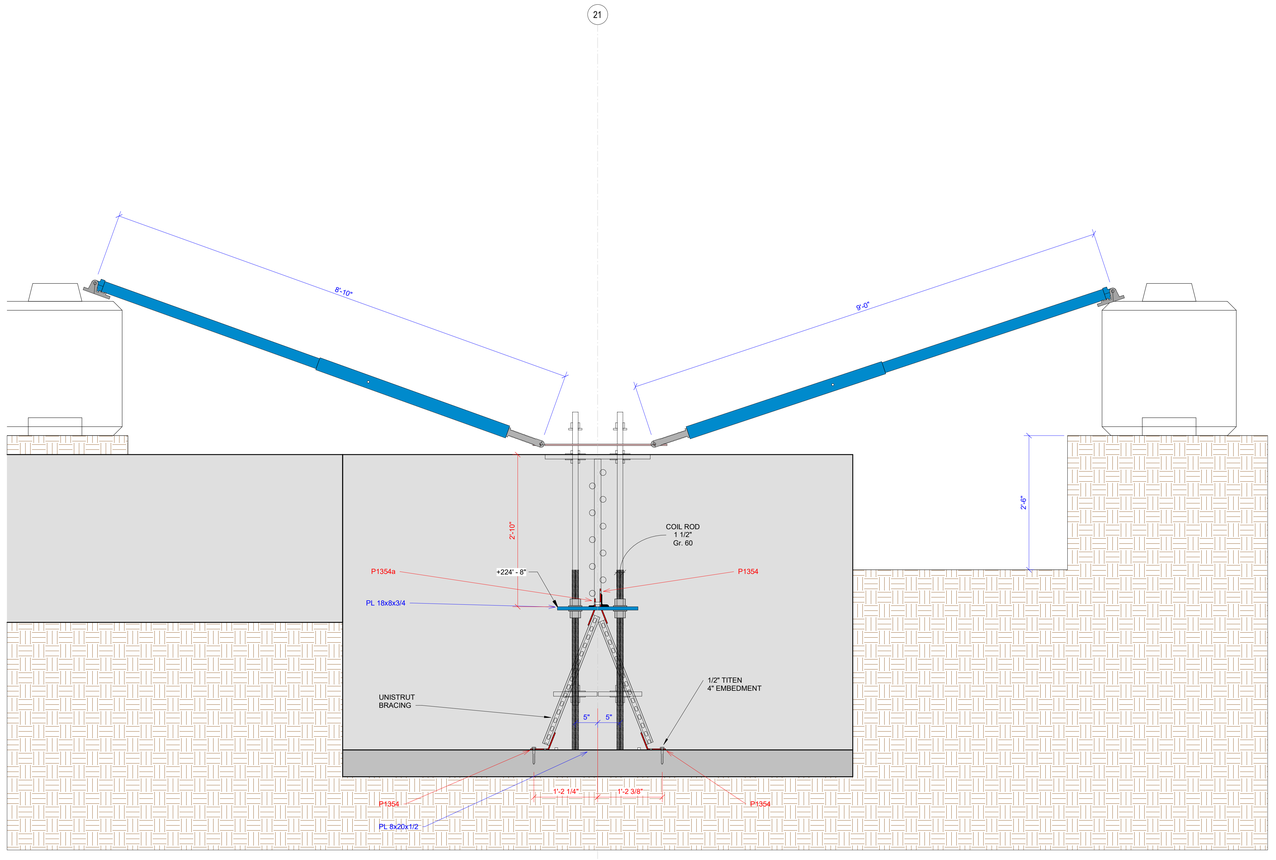


3 GL X.5/21 - N/S Copy 2 Copy 1
1" = 1'-0"

PCL CONSTRUCTION | WEBCOR
A JOINT VENTURE

San Francisco, CA 94105

WEBCOR
CONCRETE

1751 Harbor Bay Parkway, Suite 200
Alameda, CA 94502
Phone: (510) 748-1900
Fax: (510) 748-7800

LOS ANGELES CONVENTION CENTER
EXPANSION + MODERNIZATION
1201 S.FIGUEROA ST. LOS ANGELES, CA 90015

IMPORTANT NOTE:
THESE DRAWINGS ARE NOT INTENDED TO REPLACE THE DESIGN ARCHITECTURAL AND STRUCTURAL DRAWINGS. ALL DIMENSIONS, LOCATIONS, AND ELEVATIONS SHOWN ON THIS DRAWING ARE TO BE CHECKED ON-SITE AGAINST THE LATEST DESIGN AND DOCUMENTATIONS.

Revision Schedule

| Rev. No. | Revision Description | Rev. Date |
|---|---|---|
| | | |
| | | |
| | | |
| | | |
| | | |
| | | |
| | | |

Reference Documents:

| | |
|---|---|
| Drawn By: | Author |
| Date PDF Plotted: | 7/29/2026 9:55:40 AM |
| WCG Job No.: | 11088.70 |

**TITLE:**

# KPL SUPPORTS GL X.5/21 KNIFE PLATES BRACE

**SHEET NO:**

# SK-KPL SUPPORTS.X.5.21

**SCALE:** As indicated

**Z-L.D.S DRAWING SHEET NO.**
Where:
Z - ANSI SHOP DRAWING DESIGNATION
L - FLOOR LEVEL
D - DRAWING TYPE, WHERE:
0 - OVERALL PLAN
1 - SLAB PLAN
2 - SOFFIT/SUBGRADE PLAN
3 - VERTICAL PLAN
4 - CURB/TOPPING SLAB
5 - EMBED
6 - ELEVATIONS
7 - FINISH PLAN
8 - DETAILS
SL - SAFETY/LOGISTICS
PL - POINT LAYOUT
S - SHEET NO. (1,2,3, ETC if multiple pages)