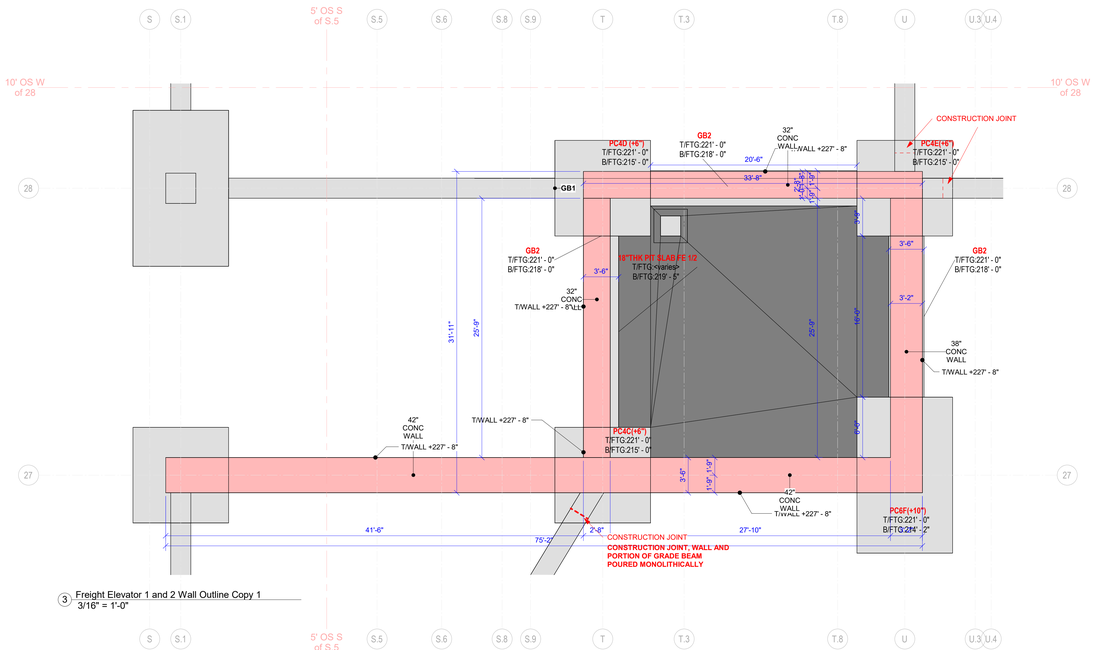
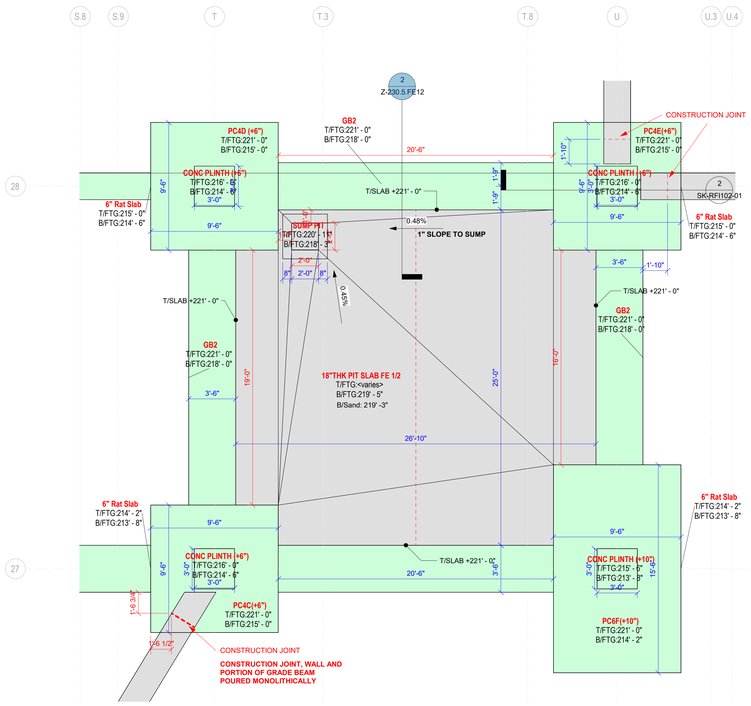
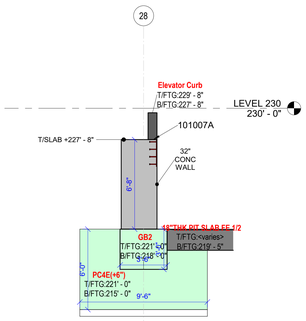


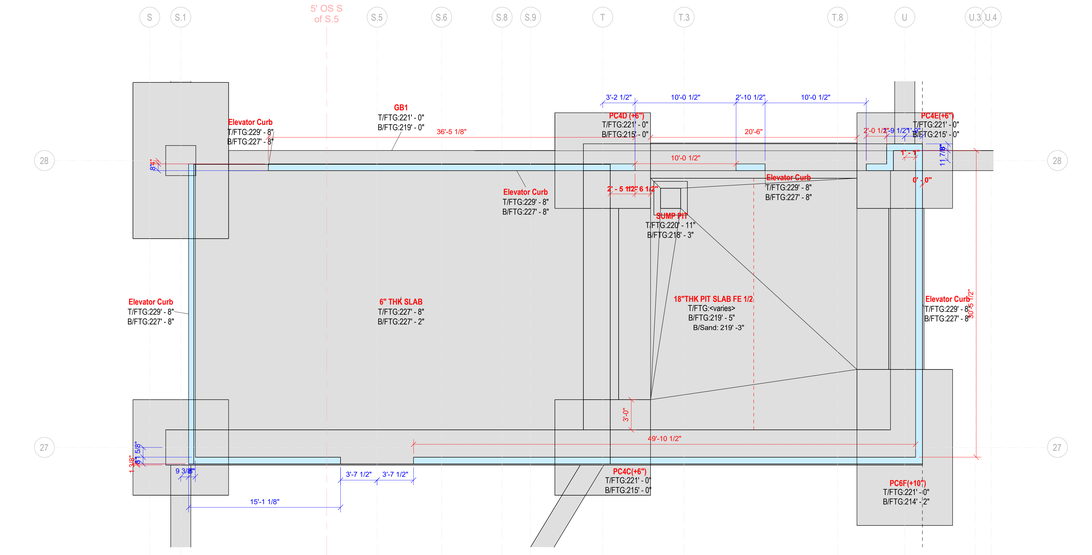

3 Freight Elevator 1 and 2 Wall Outline Copy 1
3/16" = 1'-0"



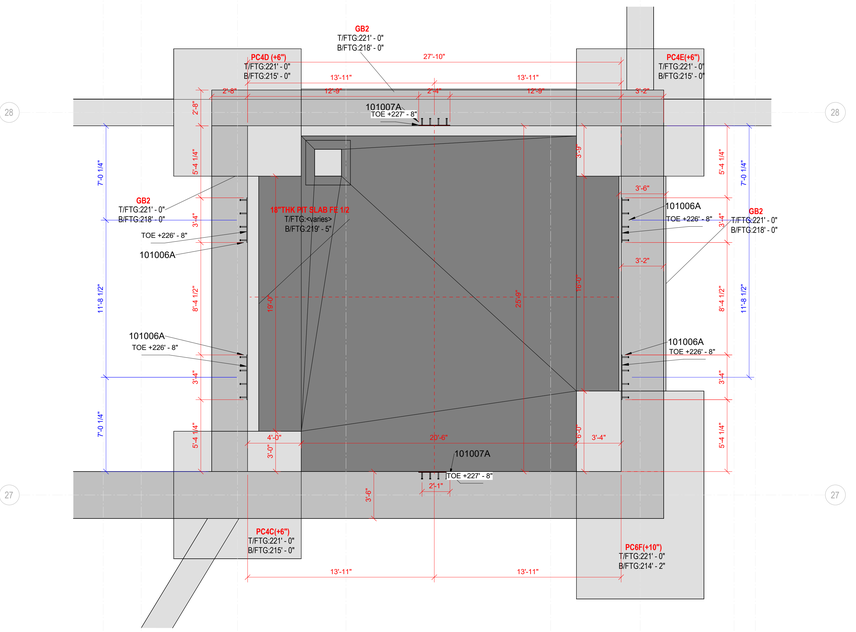

1 Freight Elevator 1 and 2 Foundation Outline Copy 1
1/4" = 1'-0"




2 Section 327 Copy 2 Copy 3
1/4" = 1'-0"




5 T/28 Elevator Curb Plan Copy 1
3/16" = 1'-0"




4 Freight Elevator 1 and 2 Embed Plan Copy 1
1/4" = 1'-0"

PCL CONSTRUCTION
A JOINT VENTURE

San Francisco, CA 94105

# LOS ANGELES CONVENTION CENTER EXPANSION + MODERNIZATION

1201 S.FIGUEROA ST. LOS ANGELES, CA 90015

IMPORTANT NOTE:
THESE DRAWINGS ARE NOT INTENDED TO REPLACE THE DESIGN ARCHITECTURAL AND STRUCTURAL DRAWINGS. ALL DIMENSIONS, LOCATIONS, AND ELEVATIONS SHOWN ON THIS DRAWING ARE TO BE CHECKED ON-SITE AGAINST THE LATEST DESIGN AND DOCUMENTATIONS.

Revision Schedule

| Rev. No. | Revision Description | Rev. Date |
|---|---|---|
| | | |
| | | |
| | | |
| | | |
| | | |
| | | |
| | | |

Reference Documents:

| | |
|---|---|
| Drawn By: | DY |
| Date PDF Plotted: | 10/6/2026 12:47:26 PM |
| WCG Job No.: | 11088.70 |

**TITLE:**

**Freight Elevator 1 and 2 OVERALL VIEW**

**SHEET NO:**

**Z-230.OV.FE12**

**SCALE:** As indicated

**Z-L.D.S DRAWING SHEET NO.**
Where:
Z - ANSI SHOP DRAWING DESIGNATION
L - FLOOR LEVEL
D - DRAWING TYPE, WHERE:
0 - OVERALL PLAN
1 - SLAB PLAN
2 - SOFFIT/SUBGRADE PLAN
3 - VERTICAL PLAN
4 - CURB/TOPPING SLAB
5 - EMBED
6 - ELEVATIONS
7 - FINISH PLAN
8 - DETAILS
SL - SAFETY/LOGISTICS
PL - POINT LAYOUT
S - SHEET NO. (1,2,3, ETC if multiple pages)