

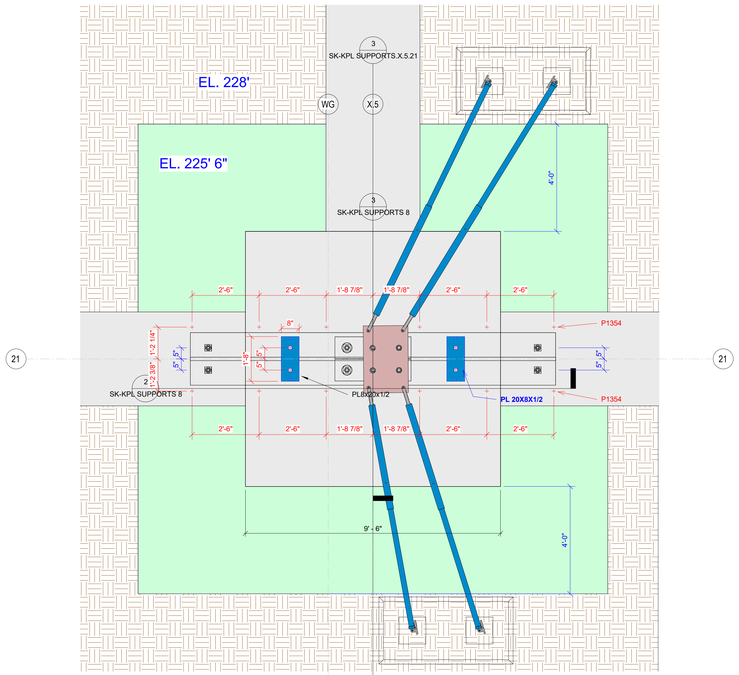


1 GL X.5/21 - LEVEL 223 Copy 2 Copy 1
1/2" = 1'-0"

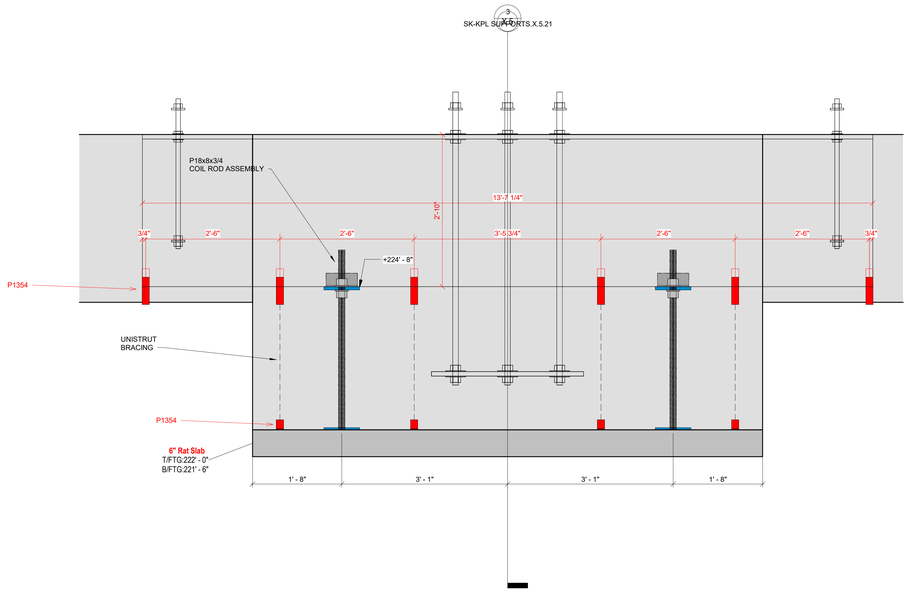

2 GL X.5/21 - E/W Copy 2 Copy 1
1" = 1'-0"

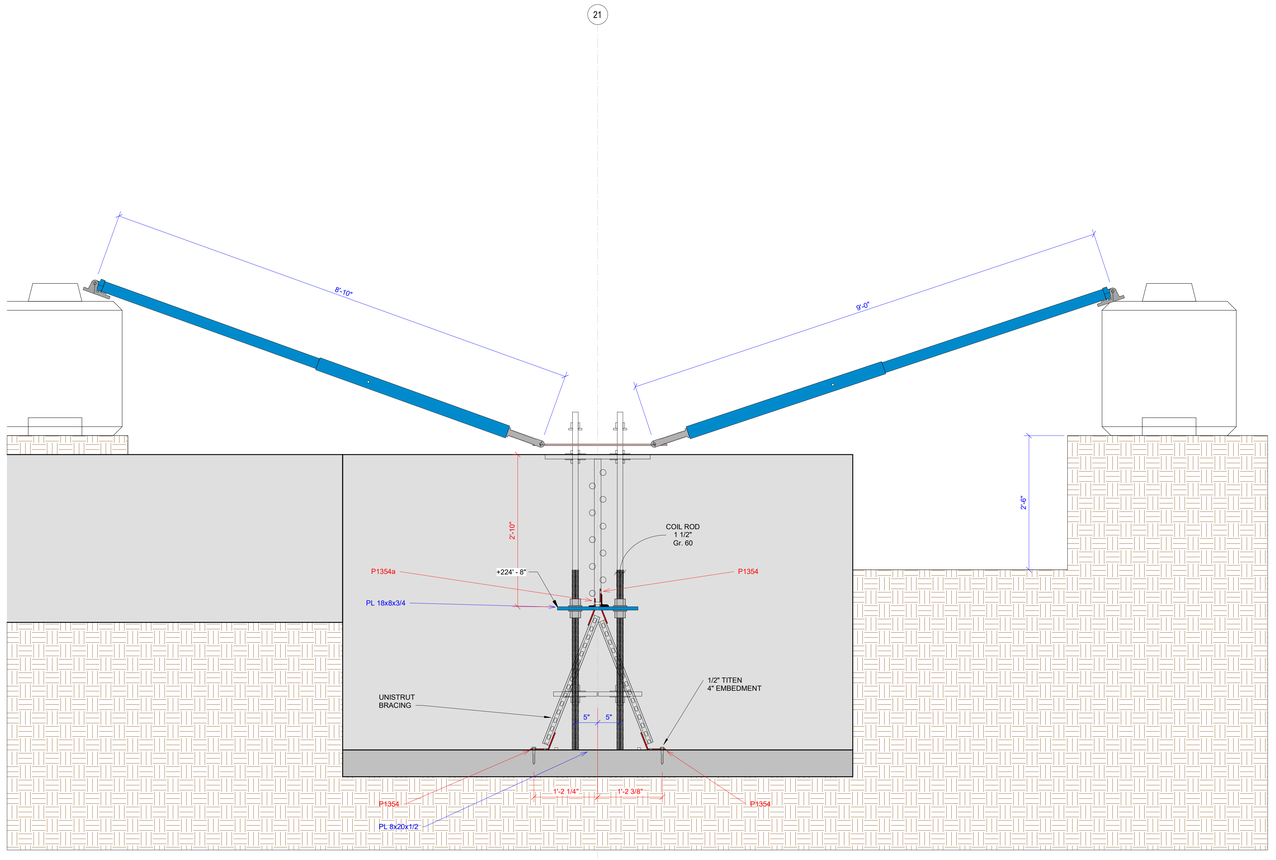

3 GL X.5/21 - N/S Copy 2 Copy 1
1" = 1'-0"

PCL CONSTRUCTION
A JOINT VENTURE
San Francisco, CA 94105

LOS ANGELES CONVENTION CENTER
EXPANSION + MODERNIZATION
1201 S.FIGUEROA ST. LOS ANGELES, CA 90015

IMPORTANT NOTE:
THESE DRAWINGS ARE NOT INTENDED TO REPLACE THE DESIGN ARCHITECTURAL AND STRUCTURAL DRAWINGS. ALL DIMENSIONS, LOCATIONS, AND ELEVATIONS SHOWN ON THIS DRAWING ARE TO BE CHECKED ON-SITE AGAINST THE LATEST DESIGN AND DOCUMENTATIONS.

Revision Schedule

Rev. No.	Revision Description	Rev. Date

Reference Documents:

Drawn By:	Author
Date PDF Plotted:	7/29/2026 9:55:40 AM
WCG Job No.:	11088.70

TITLE:

KPL SUPPORTS GL X.5/21 KNIFE PLATES BRACE

SHEET NO:

SK-KPL SUPPORTS.X.5.21

SCALE: As indicated

Z-L.D.S DRAWING SHEET NO.
Where:
Z - ANSI SHOP DRAWING DESIGNATION
L - FLOOR LEVEL
D - DRAWING TYPE, WHERE:
0 - OVERALL PLAN
1 - SLAB PLAN
2 - SOFFIT/SUBGRADE PLAN
3 - VERTICAL PLAN
4 - CURB/TOPPING SLAB
5 - EMBED
6 - ELEVATIONS
7 - FINISH PLAN
8 - DETAILS
SL - SAFETY/LOGISTICS
PL - POINT LAYOUT
S - SHEET NO. (1,2,3, ETC if multiple pages)