
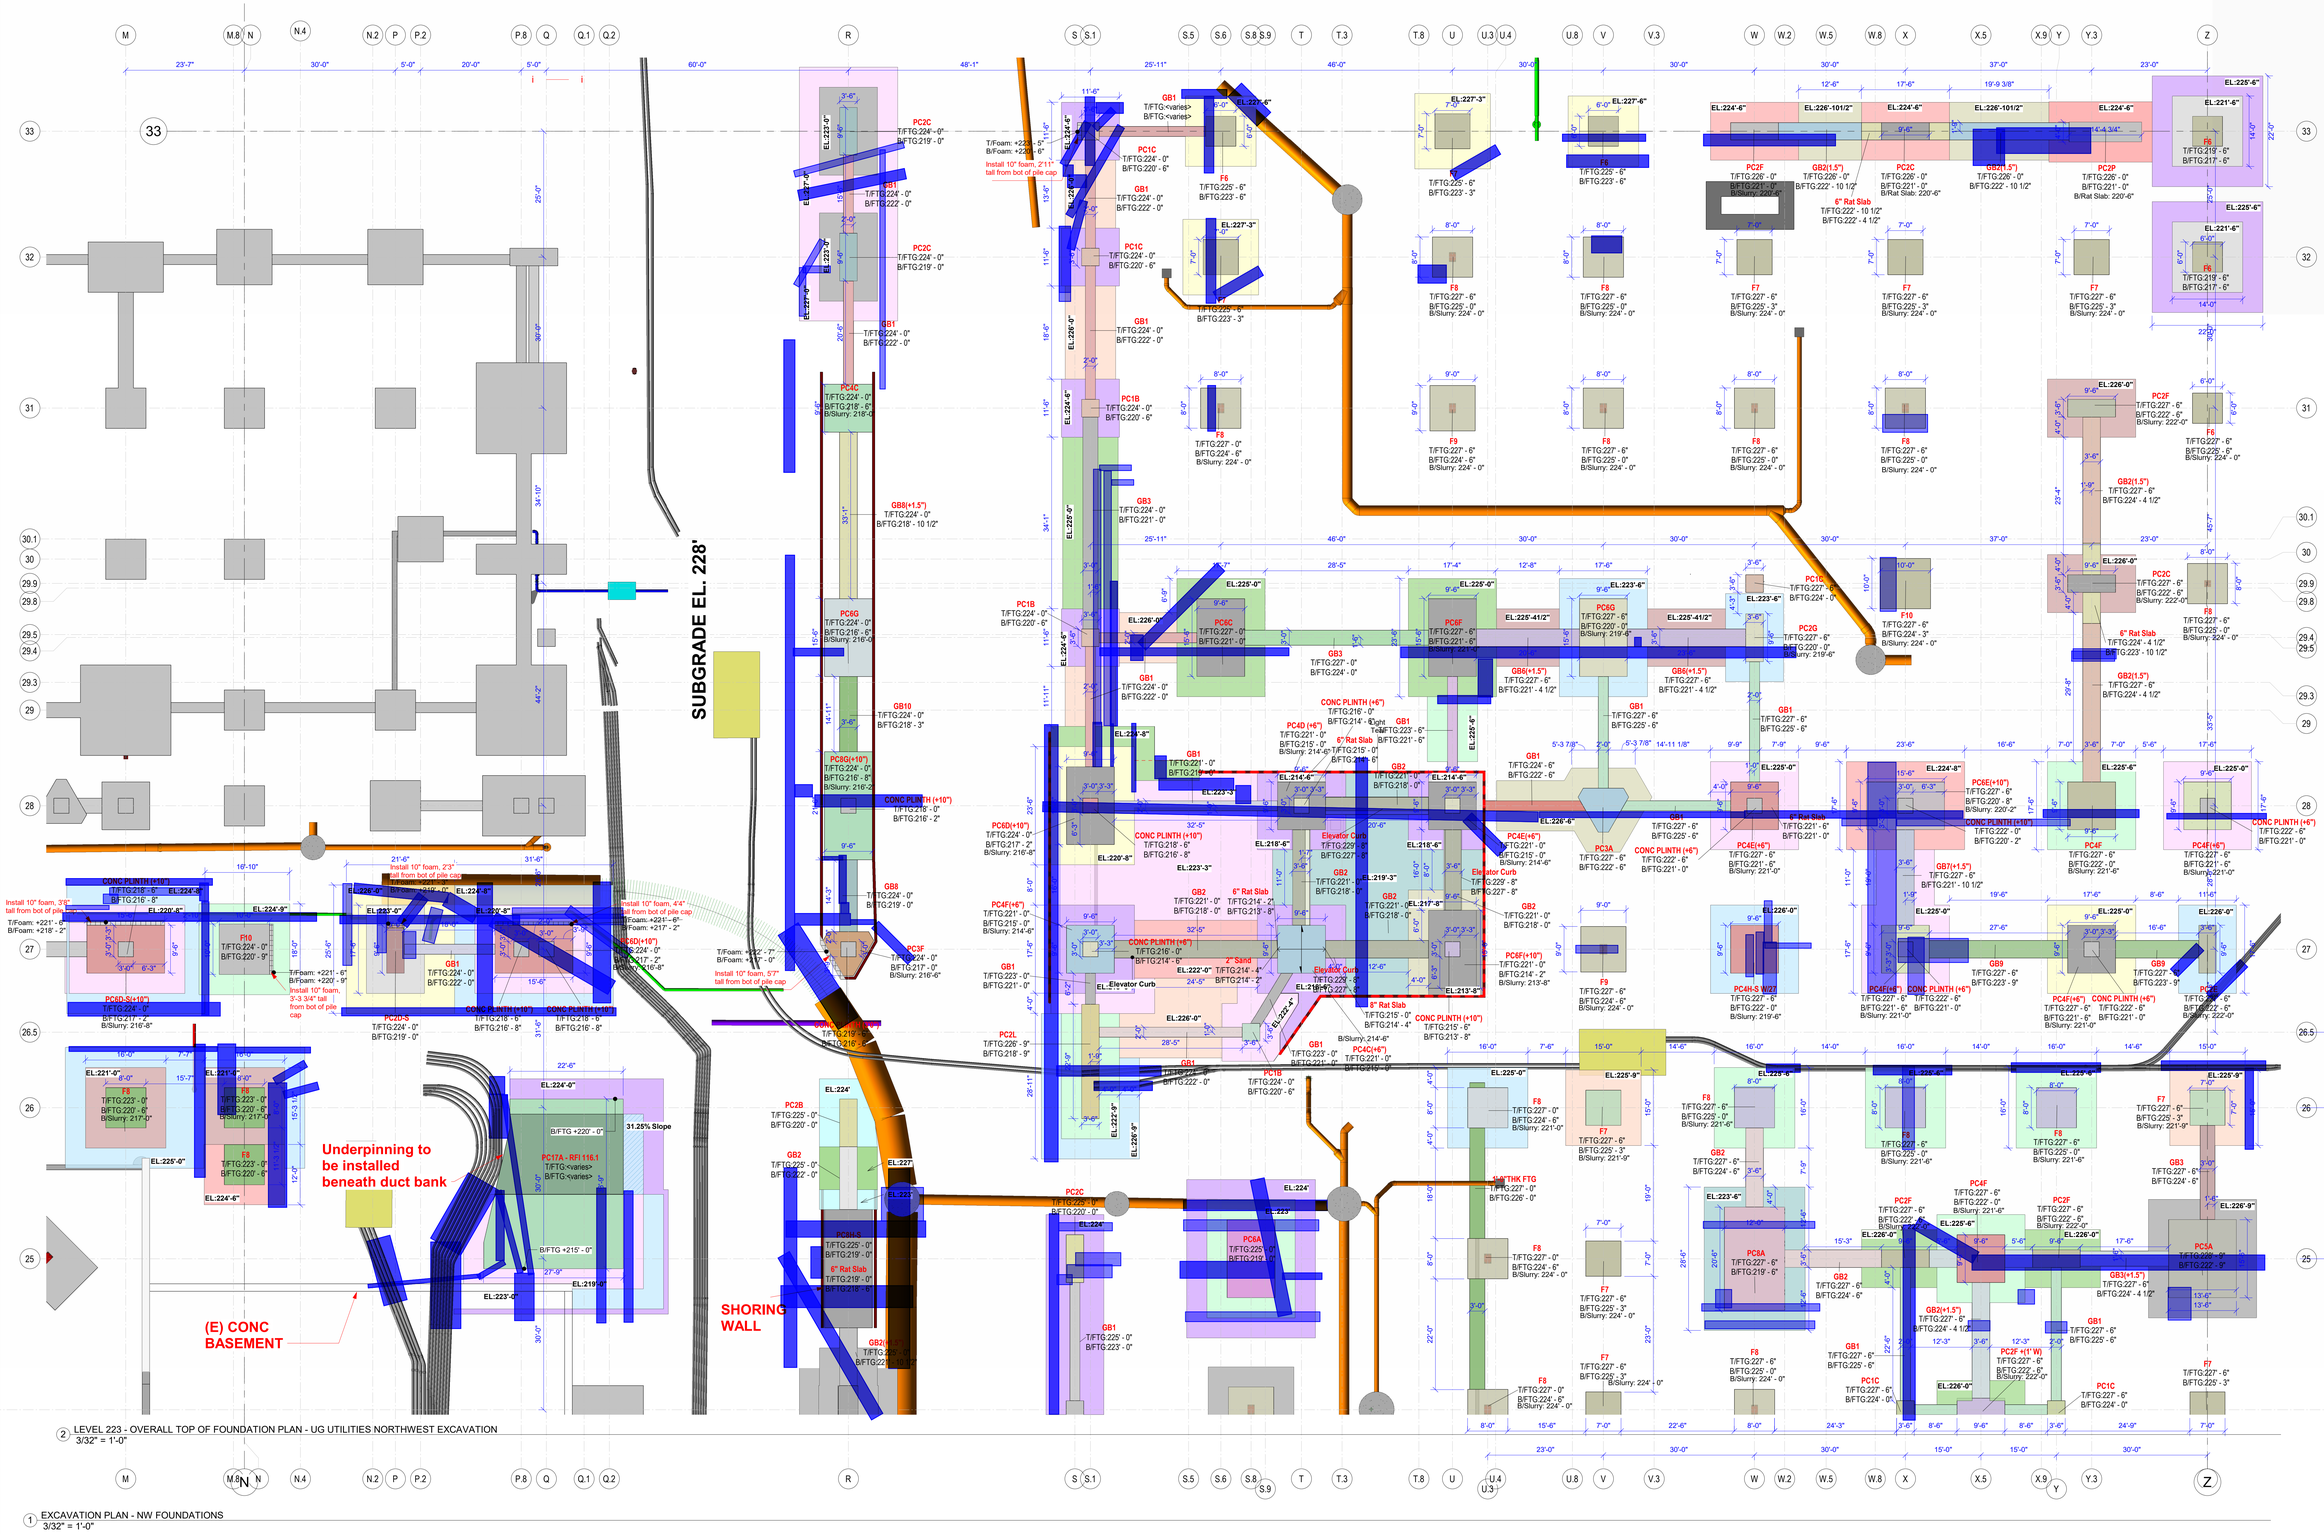


2 LEVEL 223 - OVERALL TOP OF FOUNDATION PLAN - UG UTILITIES NORTHWEST EXCAVATION
3/32" = 1'-0"

1 EXCAVATION PLAN - NW FOUNDATIONS
3/32" = 1'-0"

Excavate All Spread Footings to Native Soil

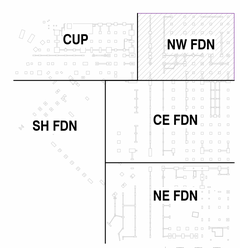

KEY PLAN

PCL CONSTRUCTION
A JOINT VENTURE

San Francisco, CA 94105

LOS ANGELES CONVENTION CENTER
EXPANSION + MODERNIZATION
1201 S.FIGUEROA ST. LOS ANGELES, CA 90015

IMPORTANT NOTE:
THESE DRAWINGS ARE NOT INTENDED TO REPLACE THE DESIGN ARCHITECTURAL AND STRUCTURAL DRAWINGS. ALL DIMENSIONS, LOCATIONS, AND ELEVATIONS SHOWN ON THIS DRAWING ARE TO BE CHECKED ON-SITE AGAINST THE LATEST DESIGN AND DOCUMENTATIONS.

Revision Schedule

Rev. No.	Revision Description	Rev. Date
3	Addednum-PH-0002	Date 3

Reference Documents:

Drawn By:	Author
Date PDF Plotted:	10/21/2026 6:58:47 AM

WCG Job No.: 11088.70

TITLE:

Excavation Plan - North West

SHEET NO:

Z-L0.2.NW.1

SCALE: 3/32" = 1'-0"

Z-L.D.S DRAWING SHEET NO.
Where:
Z - ANSI SHOP DRAWING DESIGNATION
L - FLOOR LEVEL
D - DRAWING TYPE, WHERE:
0 - OVERALL PLAN
1 - SLAB PLAN
2 - SOFFIT/SUBGRADE PLAN
3 - VERTICAL PLAN
4 - CURB/TOPPING SLAB
5 - EMBED
6 - ELEVATIONS
7 - FINISH PLAN
8 - DETAILS
SL - SAFETY/LOGISTICS
PL - POINT LAYOUT
S - SHEET NO. (1,2,3, ETC if multiple pages)